
Prilog 1: Procesni dijagram toka sa naznačenim proizvodnim cjelinama i mjestima emisija

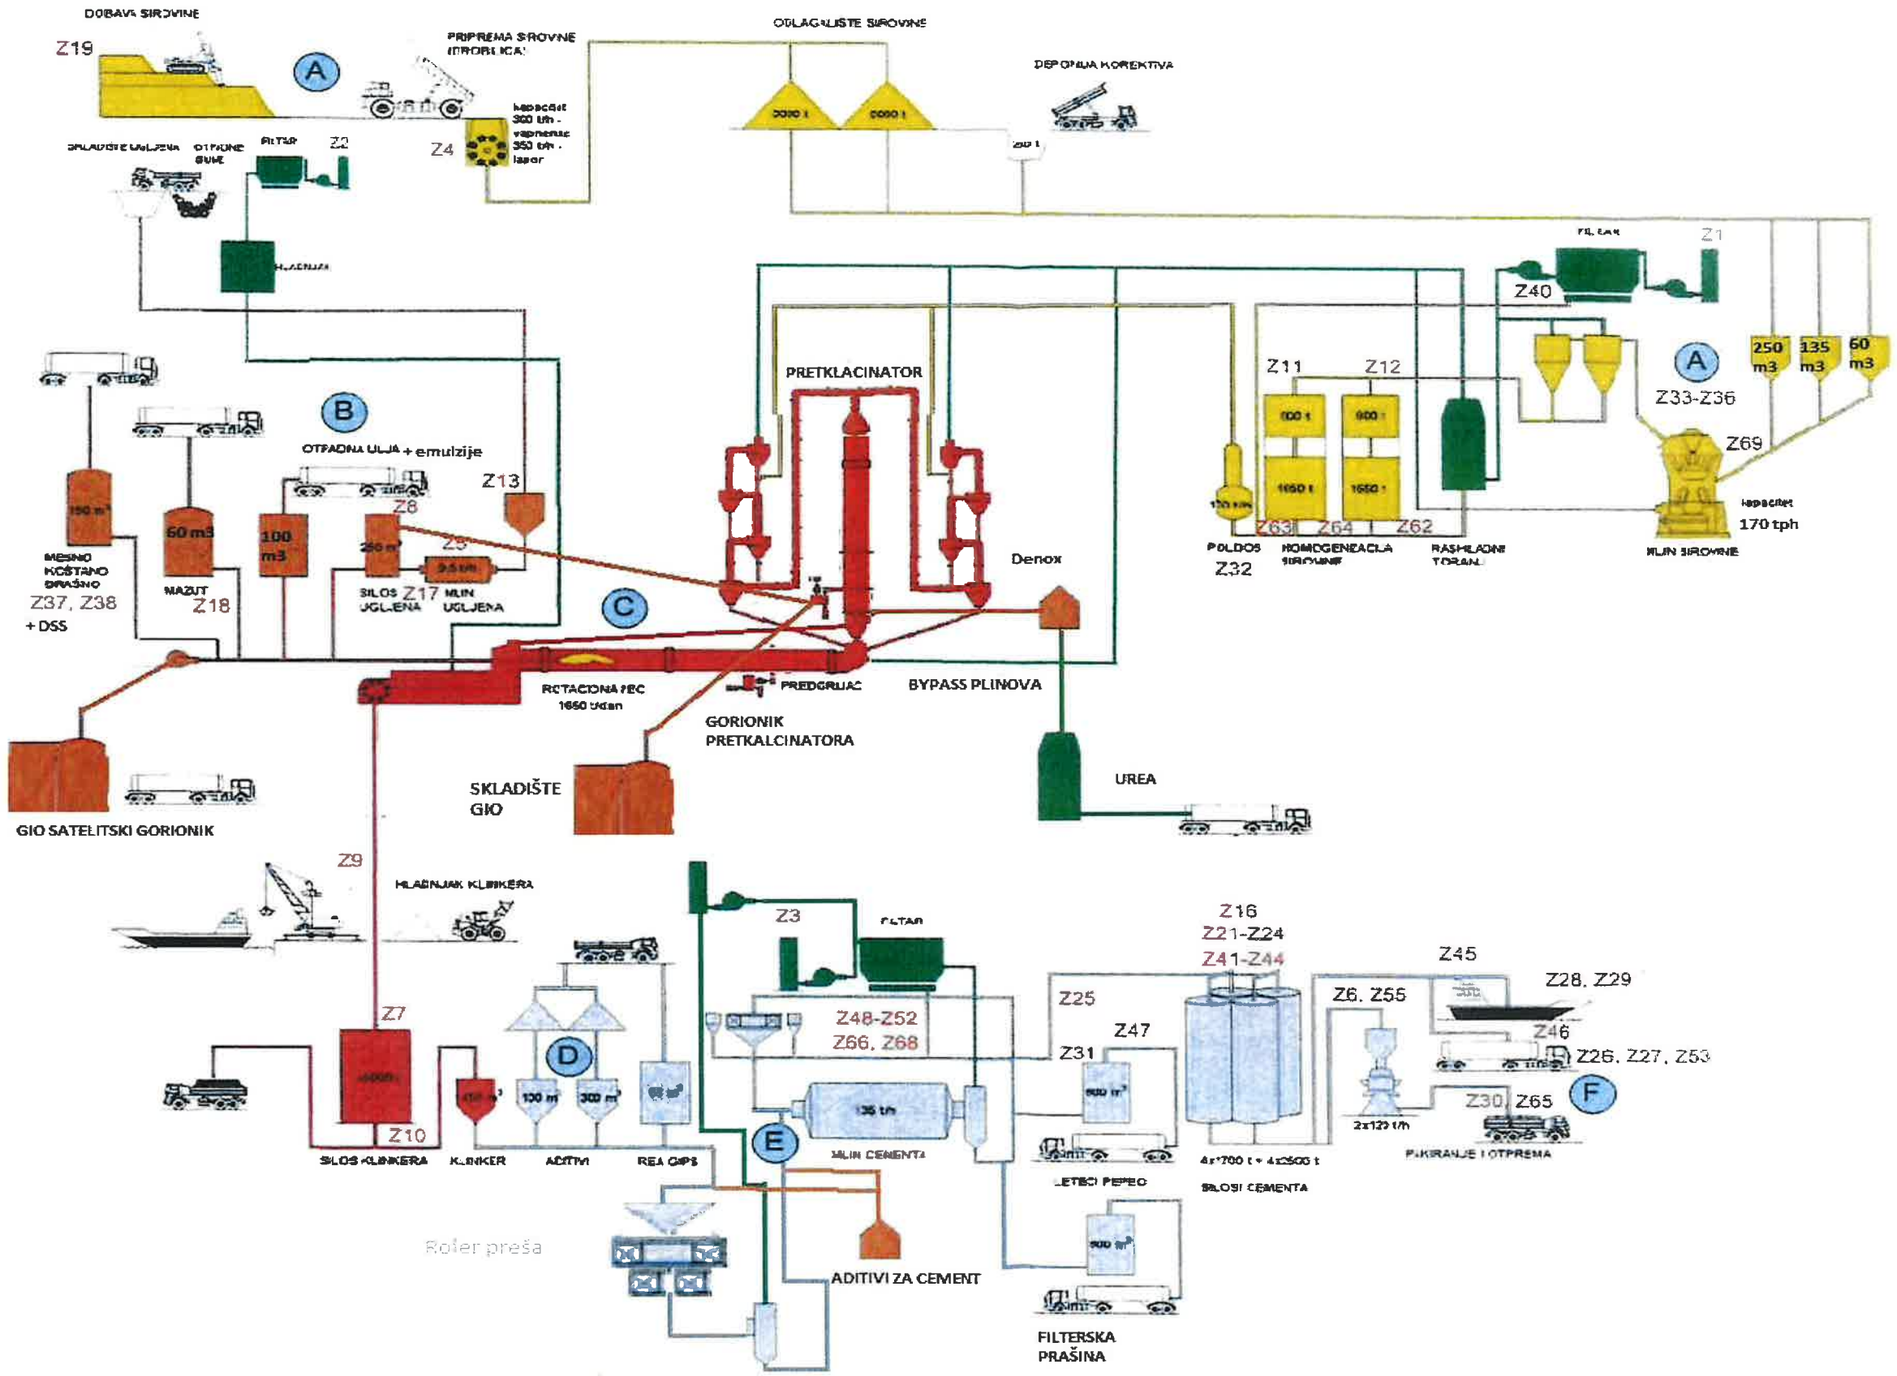

Procesni dijagram tijeka sa naznačenim proizvodnim cjelinama i mjestima emisije - Legenda


Proizvodne cjeline

A	Dobava i priprema sirovine
B	Priprema goriva
C	Proizvodnja klinkera
D	Priprema mineralnih dodataka
E	Mljevenje cementa
F	Otprema cementa

Ispusti onečišćujućih tvari u zrak

Z1	ispust vrećastog filtra rotacijske peci
Z2	otprašivač hladnjaka klinkera
Z3	dimnjak mlina cementa
Z4	otprašivač drobilice sirovine
Z5	ispust vrećastog filtra na mlinu ugljena
Z6	otprašivač pakirnice cementa
Z7	otprašivač vrha silosa klinkera
Z8	otprašivač silosa ugljene prasine
Z9	otprašivač elevatora klinkera
Z10	otprašivač dna silosa klinkera
Z11	otprašivač silosa sir. brasna SHI
Z12	otprašivač silosa sir. brasna SH2
Z13	otprasivač predbunkera m. ugljena
Z16	otprašivač 500-t silosa cementa
Z17	otprašivač fuler pumpe ml. Ugeljan
Z18	ispust iz kotlovnice peći
Z19	ispust iz kotlovnice tupinoloma
Z21	otprašivač silosa cementa br.3
Z22	otprašivač silosa cementa br.4
Z23	otprašivač silosa cementa br.5
Z24	otprašivač silosa cementa br.6
Z25	otprašivač elevatora silosa cementa
Z26	otprašivač rinfuzo ukrcaja cisterni 1 (stari)
Z27	otprašivač zr. korita za ukrcaj cisterni
Z28	otprašivač rinfuzo ukrcaja broda
Z29	otprašivač zr. korita za ukrcaj broda
Z30	otprašivač paletizatora
Z31	otprašivač silosa letećeg pepela
Z32	otprašivač Poldosa
Z33	otprašivač elevatora tilterske prašine peci
Z34	otprašivač transp. sirovine bunker-traka **1**
Z35	otprašivač transporta sirovine - presip 2/3
Z36	otprašivač elevatora povrata m.s.
Z37	otprašivač dozatora MKB-a
Z38	otprašivač silosa MKB-a
Z40	otprašivač gornjeg silosa tilt. prašine
Z41	otprašivač silosa cementa br 7
Z42	otprašivač silosa cementa br 8
Z43	otprašivač silosa cementa br 9
Z44	otprašivač silosa cementa br 10
Z45	otprašivač elevatora za ukrcaj broda
Z46	otprašivač elevatora za ukrcaj cisterni
Z47	otprašivač donjeg silosa filt. prašine
Z48	radni otprašivač prese - 541 BF1
Z49	ispust generator toplih plinova mlina cementa
Z50	otprašivač separatora mlina cementa -561 BF2
Z51	otprašivač transporta klinkera, troske i vapnenca (Vaga-elevator) – 541 BF4/BF5
Z52	otprašivač transporta materijala do i od preše 541 BF2/BF3
Z53	otprašivač rinfuzo ukrcaja cisterni 2 (novi)
Z55	otprašivač transporta u pakirnicu cementa
Z62	otprašivač silosa sir.brašna SD2
Z63	otprašivač silosa sir.brašna SD1
Z64	otprašivač transporta sir.brašna iz silosa
Z65	otprašivač vreća pakiranog cementa
Z66	otprašivač usipa u bunker preše – 541 BF7
Z67*	otprašivač bunkera preše – 541 BF7
Z68	otprašivač metalnog otpada – 541 BF97
Z69	otprašivač transporta sirovine -presip 1/2

Prilog 2. Plan s prikazom lokacije zahvata s granicama obuhvata cijelog postrojenja (situacija)

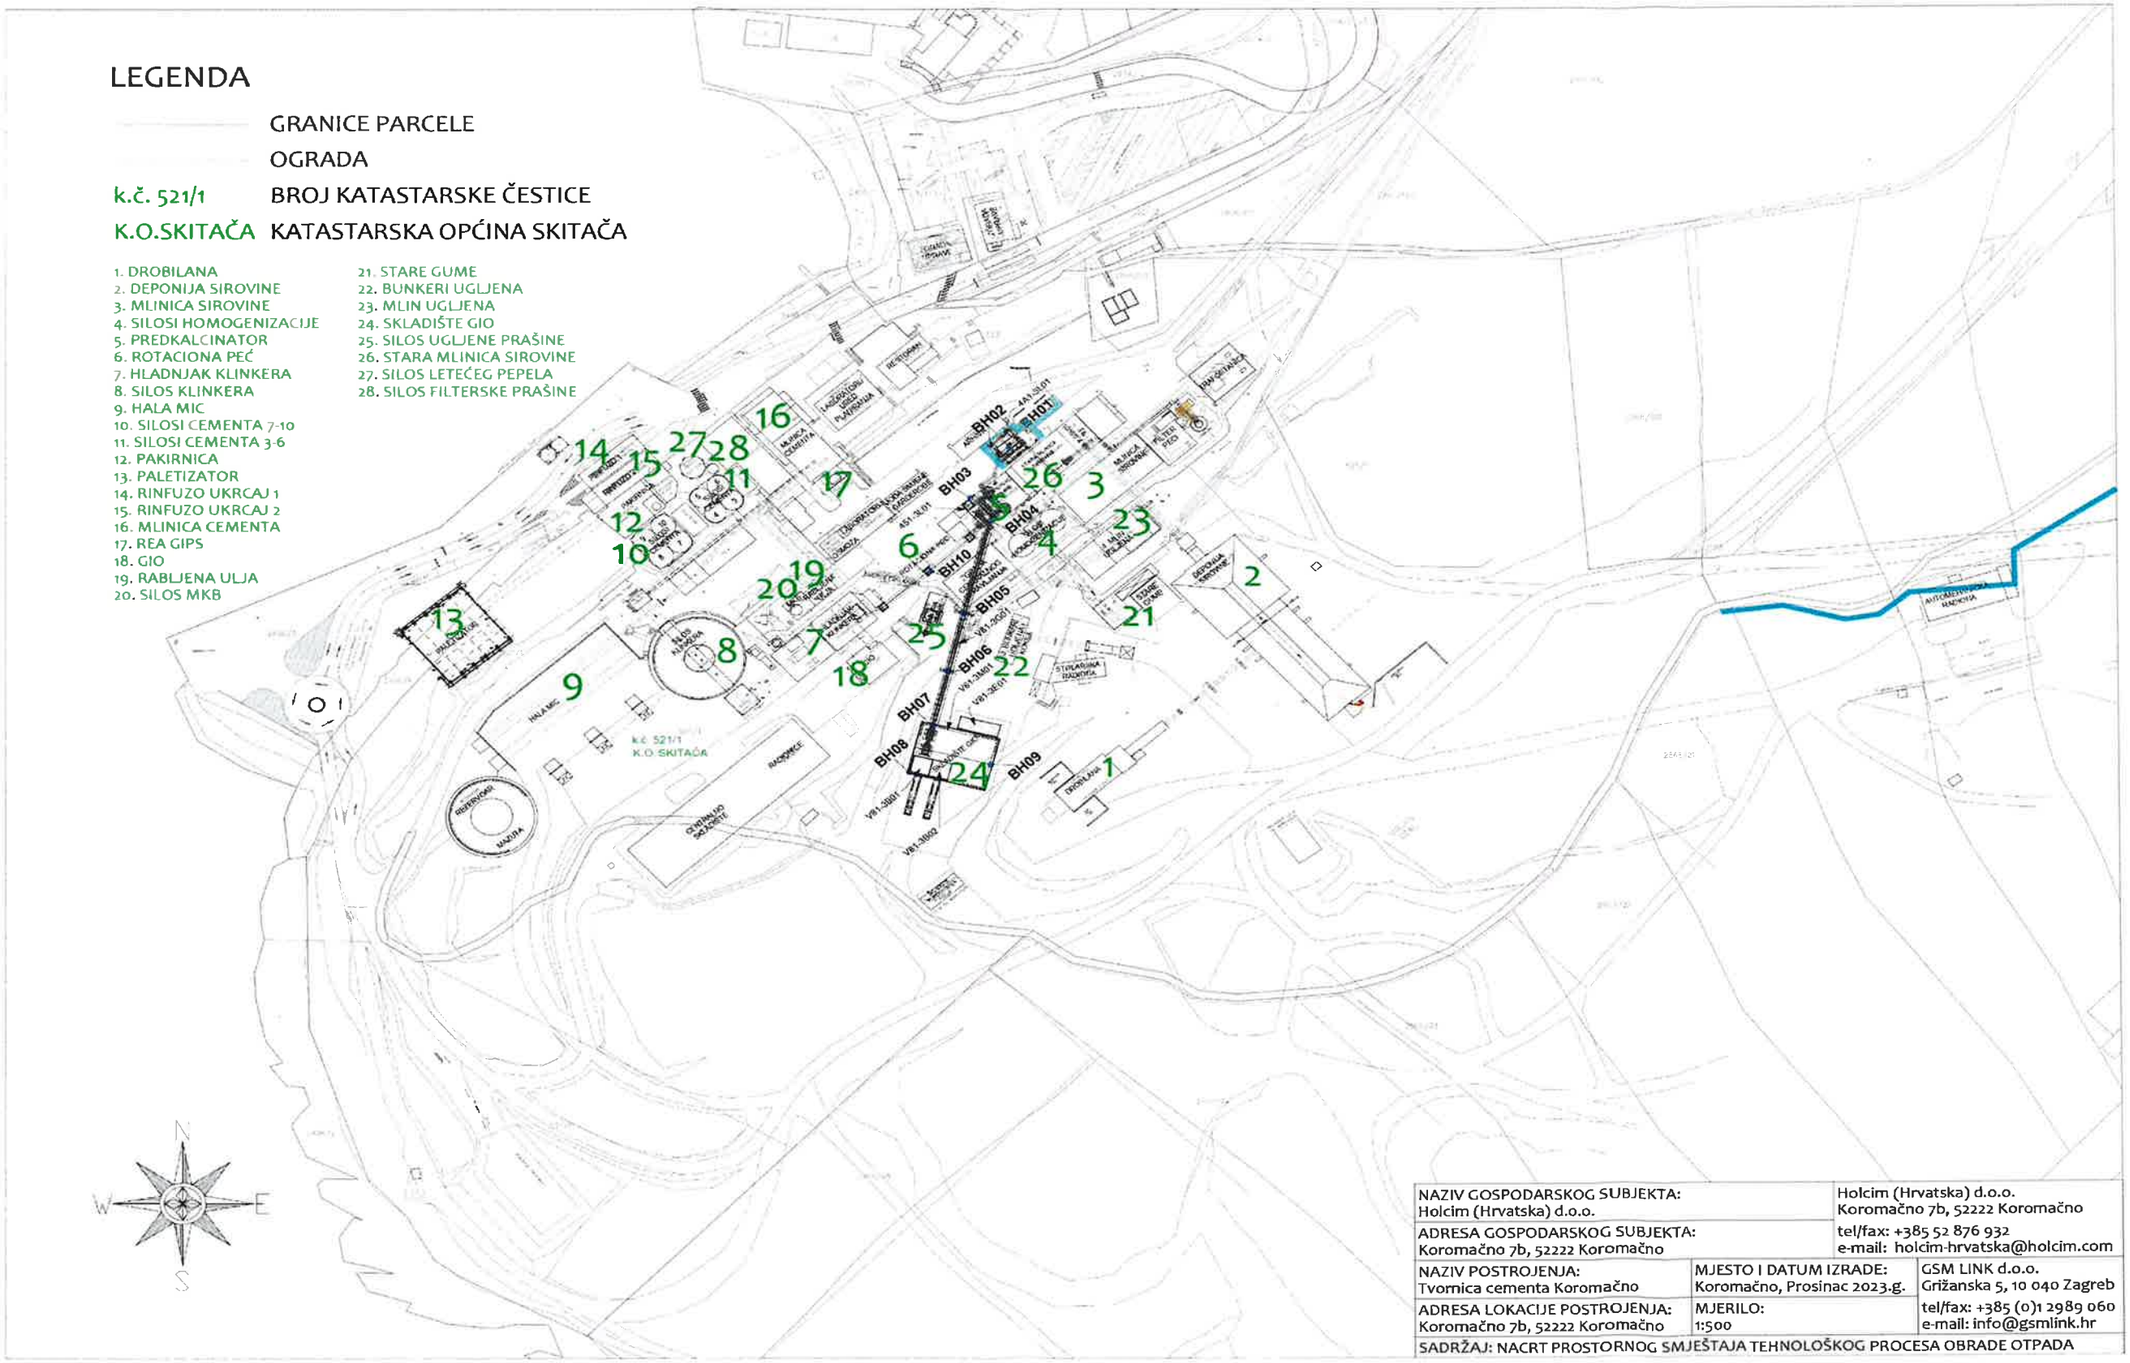

NAZIV GOSPODARSKOG SUBJEKTA: Holcim (Hrvatska) d.o.o.		Holcim (Hrvatska) d.o.o. Koromačno 7b, 52222 Koromačno
ADRESA GOSPODARSKOG SUBJEKTA: Koromačno 7b, 52222 Koromačno		tel/fax: +385 52 876 932 e-mail: holcim-hrvatska@holcim.com
NAZIV POSTROJENJA: Tvornica cementa Koromačno	MJESTO I DATUM IZRADE: Koromačno, Prosinac 2023.g.	GSM LINK d.o.o. Grižanska 5, 10 040 Zagreb
ADRESA LOKACIJE POSTROJENJA: Koromačno 7b, 52222 Koromačno	MJERILO: 1:500	tel/fax: +385 (0)1 2989 060 e-mail: info@gsmlink.hr
SADRŽAJ: NACRT PROSTORNOG SMJEŠTAJA TEHNOLOŠKOG PROCESA OBRADE OTPADA		